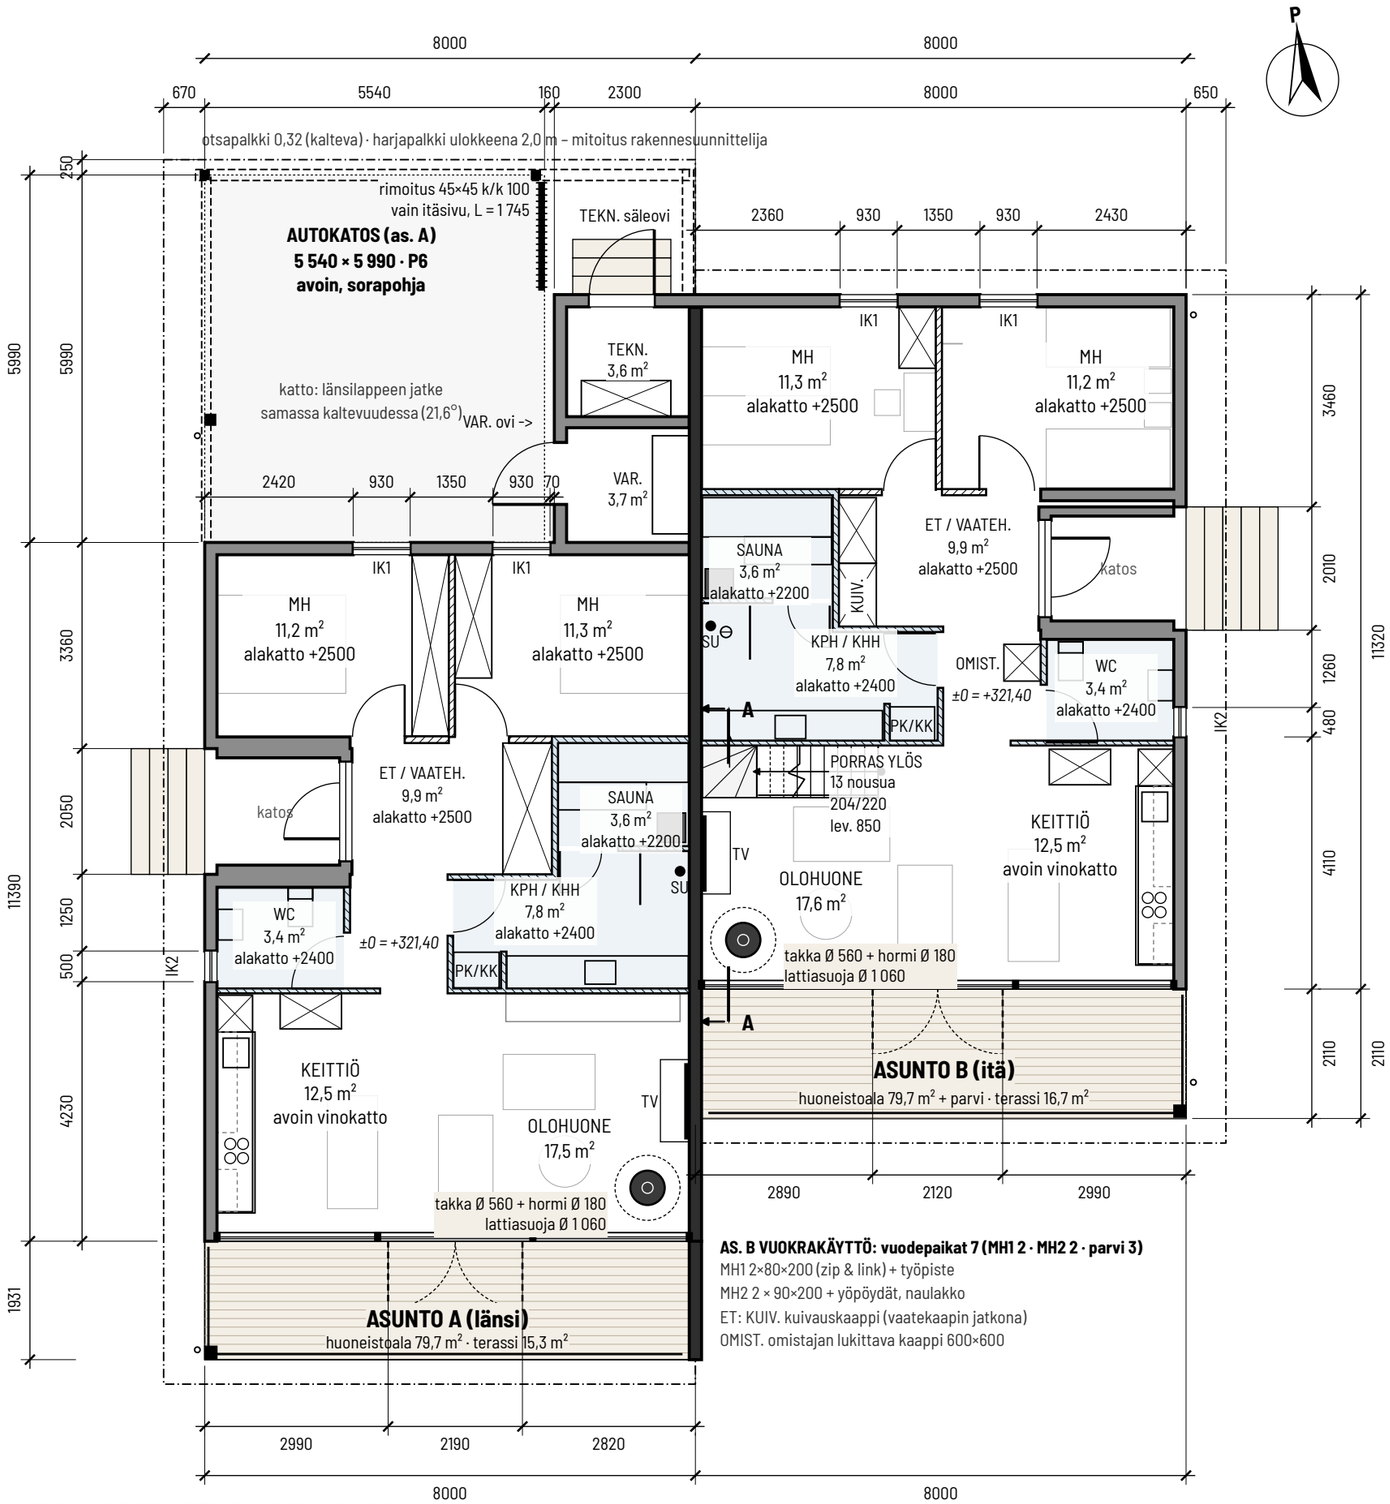


AS. B VUOKRAKÄYTTÖ: vuodepaikat 7 (MH1 2 · MH2 2 · parvi 3)
MH1 2×80×200 (zip & link) + työpiste
MH2 2 × 90×200 + yöpöydät, naulakko
ET: KUIV. kuivauskaappi (vaatekaapin jatkona)
OMIST. omistajan lukittava kaappi 600×600

POHJAPIIRUSTUS 1. KRS 1:100

Mitat millimetreinä 3D-mallista (ulkoseinän ulkopinnat; ulkoseinä puurunko + hirsipaneeliverhous, ks. B04). Korot: ±0 = 1. krs lattia (+321,40 N2000, MML DEM -tarkistettu – mittaus tark.).

0 1 2 3 4 5 m

MITTAKAAVA 1:100 (A3)

Kalusteet harmaalla ohjeellisia. Ovien aukeamissuunnat ja kiintokalusteet tarkentuvat. Leikkaus A–A: lehti 2.

PINTA-ALAT (m², 3D-mallin sisämitoista)

Tila	As. A	As. B
Makuuhuone	11,2	11,3
Makuuhuone	11,3	11,2
Eteinen	9,9	9,9
Sauna (märkätila)	3,6	3,6
Kylpyhuone / kodinhoito (märkätila)	7,8	7,8
WC (märkätila)	3,4	3,4
Keittiö	12,5	12,5
Olohuone	17,5	17,6
Huonealat yhteensä	77,4	77,4
Huoneistoala 1. krs (sisäpinnoista)	79,7	79,7
Parvi, vapaa korkeus ≥ 1,6 m		16,4
Parvi, vapaa korkeus < 1,6 m		11,8
Terassi (avoin, katettu osin)	15,3	16,7
Autokatos (avoin)	33,2	

Tekninen tila 3,6 + varasto 3,7 m² (ulkokautta, varastosiipi)
A/B huoneet peilikuvia (u→16–u, v→v–4,04). B:n erot: parviporras OH:ssa (kuuluu huoneistoalaan), takka OH-nurkassa (B lounais, A kaakko), keittiöt yhtä pitkät (ei muuta huonepolygonia).

KERROSALA (ulkoseinien ulkopinnoista)

1. krs, 3D-malli	182,0
1. krs, valmistajan ilmoitus (Honka)	183,5
Parvi as. B, osa ≥ 1,6 m	16,4
Yhteensä (malli / valmistaja)	**198,5 / 199,9 k-m²**
Rakennusoikeus (kaava, lähdeaineisto)	200 k-m² + t40
Kokonaisala n. (1. krs + koko parvi)	210,2 m²

Huom. marginaali rakennusoikeuteen vain 0,1–1,6 k-m². Parven laskentatapa (kaavamerkintä ½k l u¾) ja kerrosala tarkistetaan rakennusvalvonnasta.

SEINÄTYYPIT JA MERKINNÄT

- US1 ulkoseinä, puurunko + hirsipaneeli (ks. B04) – energiaselvitys tark.
- HVS huoneistojen välinen seinä 200 (EI 60, ääneneristys R'w ≥ 55 dB tark.)
- VS2 kevyt väliseinä n. 100
- VS3 märkätilan väliseinä 70–100, vedeneristys
- märkätilan lattia (alakatto merkitty huonetietoon)
- räystäslinja / katon ulkoreuna
- katoksen palkit, yläkaapit, aukot yläpuolella

IK1 ikkuna 930×1560 (yläreuna +2,32, alakaton alla) · IK2 ikkuna kph/wc 500×1520 (as. A) / 480×1560 (as. B)
PK/KK pesukone/kuivauskaappi · SU suihku/lattiakaivo · pieni ympyrä = syöksytorvi

HUOMAUTUKSET (tarkistettavat)

0. Sisäkorkeudet: OH+keittiö avoin vinokatto; MH/eteinen +2,50; KPH/WC +2,40; sauna +2,20; parvi +2,65 (rakenne 0,15).
1. Parviporras 13 × 204 / 220 (n. 43°), lev. 850, 9 suoraa + 4 kääntöä yläpäässä (KPH-seinä); kääntöjen kulkulinja ~196 mm – tarkista tarkistetaan (YMa 1007/2017) ja tarvittaessa muutetaan.
2. Ulkoportaat: maanpinta (DEM) n. 0,65–1,15 m lattian alapuolella; as. B ulko-ovi alin askelma 0,24 m maasta – ulkoportaat, tasanteet ja kaiteet tarkennetaan.
3. Takka Ø 560 (musta): B OH lounaisnurkka, runko 400 HVS-seinästä; A kaakkoisnurkka 400 ulkoseinästä; hormi Ø 180 pystysuoraan 0,78 m harjasta, piippu +7,36 (0,8 m harjan yli); suojaetäisyydet, HVS-osastointi valmistajan ohjeen mukaan.
4. Huoneistojen välinen seinä, palo- ja ääneneristys: rakennesuunnittelija.
5. Mitat 3D-mallista; Honka: leveys 15 996, kerrosala 183,5 m², terassit 14,2 m².

LUONNOS – ei rakennuslupakelpoinen ennen suunnittelijan tarkastusta ja allekirjoitusta

RAKENNUSKOHDE

Paritalo, 2 loma-asuntoa – Honka Joiku 184, versio B

RAKENNUSPAIKKA / OSOITE	RAKENNUSTOIMENPIDE
Siimapolku, tontti 4 (kortteli 199a), Ruka, Kuusamo – katuosoite tark.	Uudisrakennus


PIIRUSTUKSEN SISÄLTÖ

PÄÄPIIRUSTUS – POHJAPIIRUSTUS 1. KRS

MITTAKAAVA	PÄIVÄYS	VERSIO	PIIRUSTUSNUMERO / LEHTI
1:100	19.10.2026	B2	_____ lehti 1/3

KUNTA / KIINTEISTÖTUNNUS	RAKENNUSLUPATUNNUS
Kuusamo (305) / ____-___-____-____	
PÄÄSUUNNITTELIJA (nimi, tutkinto, allekirjoitus)	RAKENNUSSUUNNITTELIJA (nimi, tutkinto, allekirjoitus)
MUUTOKSET B2 19.10.2026: maasto MML DEM, tiet, rummut, itäpiha; IK1 → 930×1560 B1 19.10.2026: porras KPH-seinä, itä P1–P2 + jätekatos, korkeusaudit	LÄHTÖTIEDOT 3D-malli joiku_versio_b.blend (huonealat-peilaus 19.10.2026) Honka Joiku 184; A/B peilikuvat; B: parvi v8 + takka OH-nurkka

PARVITASO 1:100

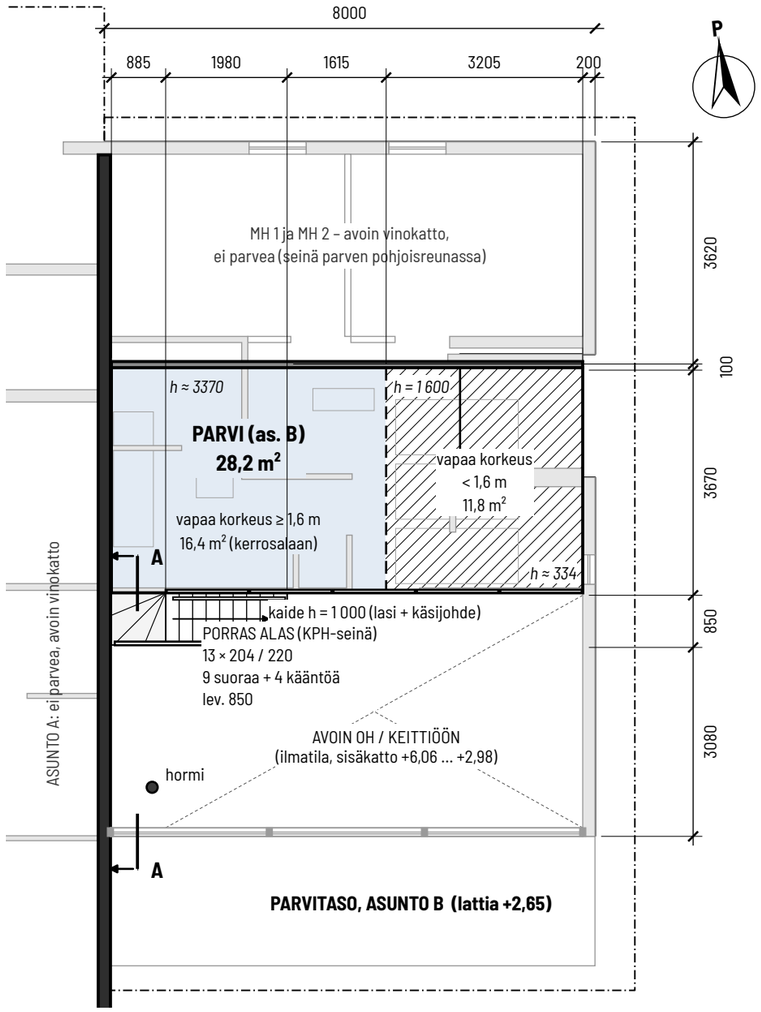

Parven alue: ≥ 1,6 m sininen, < 1,6 m vinoviivoitettu, 1,6 m raja katkoviivalla.
Alakerta harmaalla. Mitat mm (3D-malli). Leikkaus A–A oikealla.


PARVEN ALAT (3D-malli, parvi v8)

Parvi yhteensä (suorakaide)	28,2 m²
vapaa korkeus ≥ 1,6 m (kerrosalaan)	16,4 m²
vapaa korkeus < 1,6 m	11,8 m²
Vapaa korkeus max / min	3,37 / 0,33 m
Parven lattia / alapinta	+2,65 / +2,50
Porras	13 × 204 / 220 mm, 43°, lev. 850
Kerrosala yht. (1. krs malli / Honka + parvi)	198,5 / 199,9 k-m²

0 1 2 3 4 5 m

MITTAKAAVA 1:100 (A3)

LEIKKAUS A–A 1:50 (portaan kohdalta, katsottuna länteen)

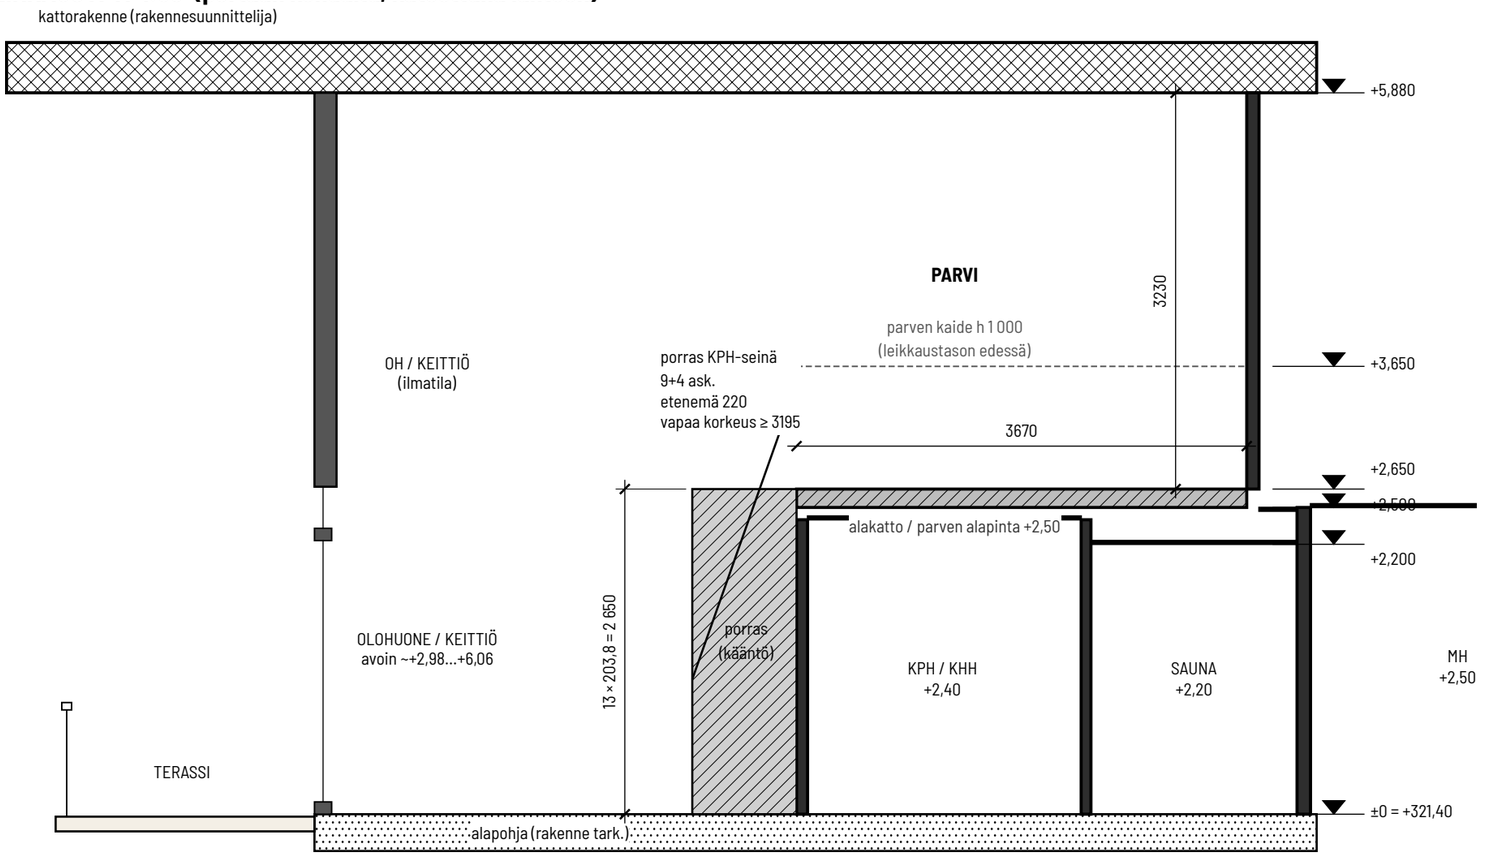

Pohjoinen oikealla. Ulkoseinät, perustukset ja maanpinta: ks. pohja 1:100 ja asemapiirros.

0 0.5 1 1.5 2 2.5 3 m

MITTAKAAVA 1:50 (A3)

HUOMAUTUKSET

1. Porras: etenemä 210 < 220 ja jyrkkyys n. 44° – mitoitus tarkistetaan (YMa 1007/2017 4 §) ennen lupaa.
2. Parven kerrosalaan laskettava osa (≥ 1,6 m) ja kaavan ½k-merkintä tarkistetaan rakennusvalvonnasta.
3. Parven kantava rakenne, kaiteet ja paloturvallisuus: rakennesuunnittelija / pääsuunnittelija.
4. Korot N2000: MML 2 m korkeusmalli (±0 = +321,40) – mittaus tark.

LUONNOS – ei rakennuslupakelpoinen ennen suunnittelijan tarkastusta ja allekirjoitusta

RAKENNUSKOHDE

Paritalo, 2 loma-asuntoa – Honka Joiku 184, versio B

RAKENNUSPAIKKA / OSOITE	RAKENNUSTOIMENPIDE
Siimapolku, tontti 4 (kortteli 199a), Ruka, Kuusamo – katuosoite tark.	Uudisrakennus


PIIRUSTUKSEN SISÄLTÖ

PÄÄPIIRUSTUS – PARVITASO 1:100, LEIKKAUS A–A 1:50

MITTAKAAVA	PÄIVÄYS	VERSIO	PIIRUSTUSNUMERO / LEHTI
1:100 / 1:50	19.10.2026	B2	_____ lehti 2/3

KUNTA / KIINTEISTÖTUNNUS	RAKENNUSLUPATUNNUS
Kuusamo (305) / ____-___-____-____	
PÄÄSUUNNITTELIJA (nimi, tutkinto, allekirjoitus)	RAKENNUSSUUNNITTELIJA (nimi, tutkinto, allekirjoitus)
MUUTOKSET B2 19.10.2026: maasto MML DEM, tiet, rummut, itäpiha; IK1 → 930×1560 B1 19.10.2026: porras KPH-seinä, itä P1–P2 + jätekatos, korkeusaudit	LÄHTÖTIEDOT 3D-malli joiku_versio_b.blend (huonealat-peilaus 19.10.2026) Honka Joiku 184; A/B peilikuvat; B: parvi v8 + takka OH-nurkka

ASEMAPIIRROS JA PIHASUUNNITELMA 1:200

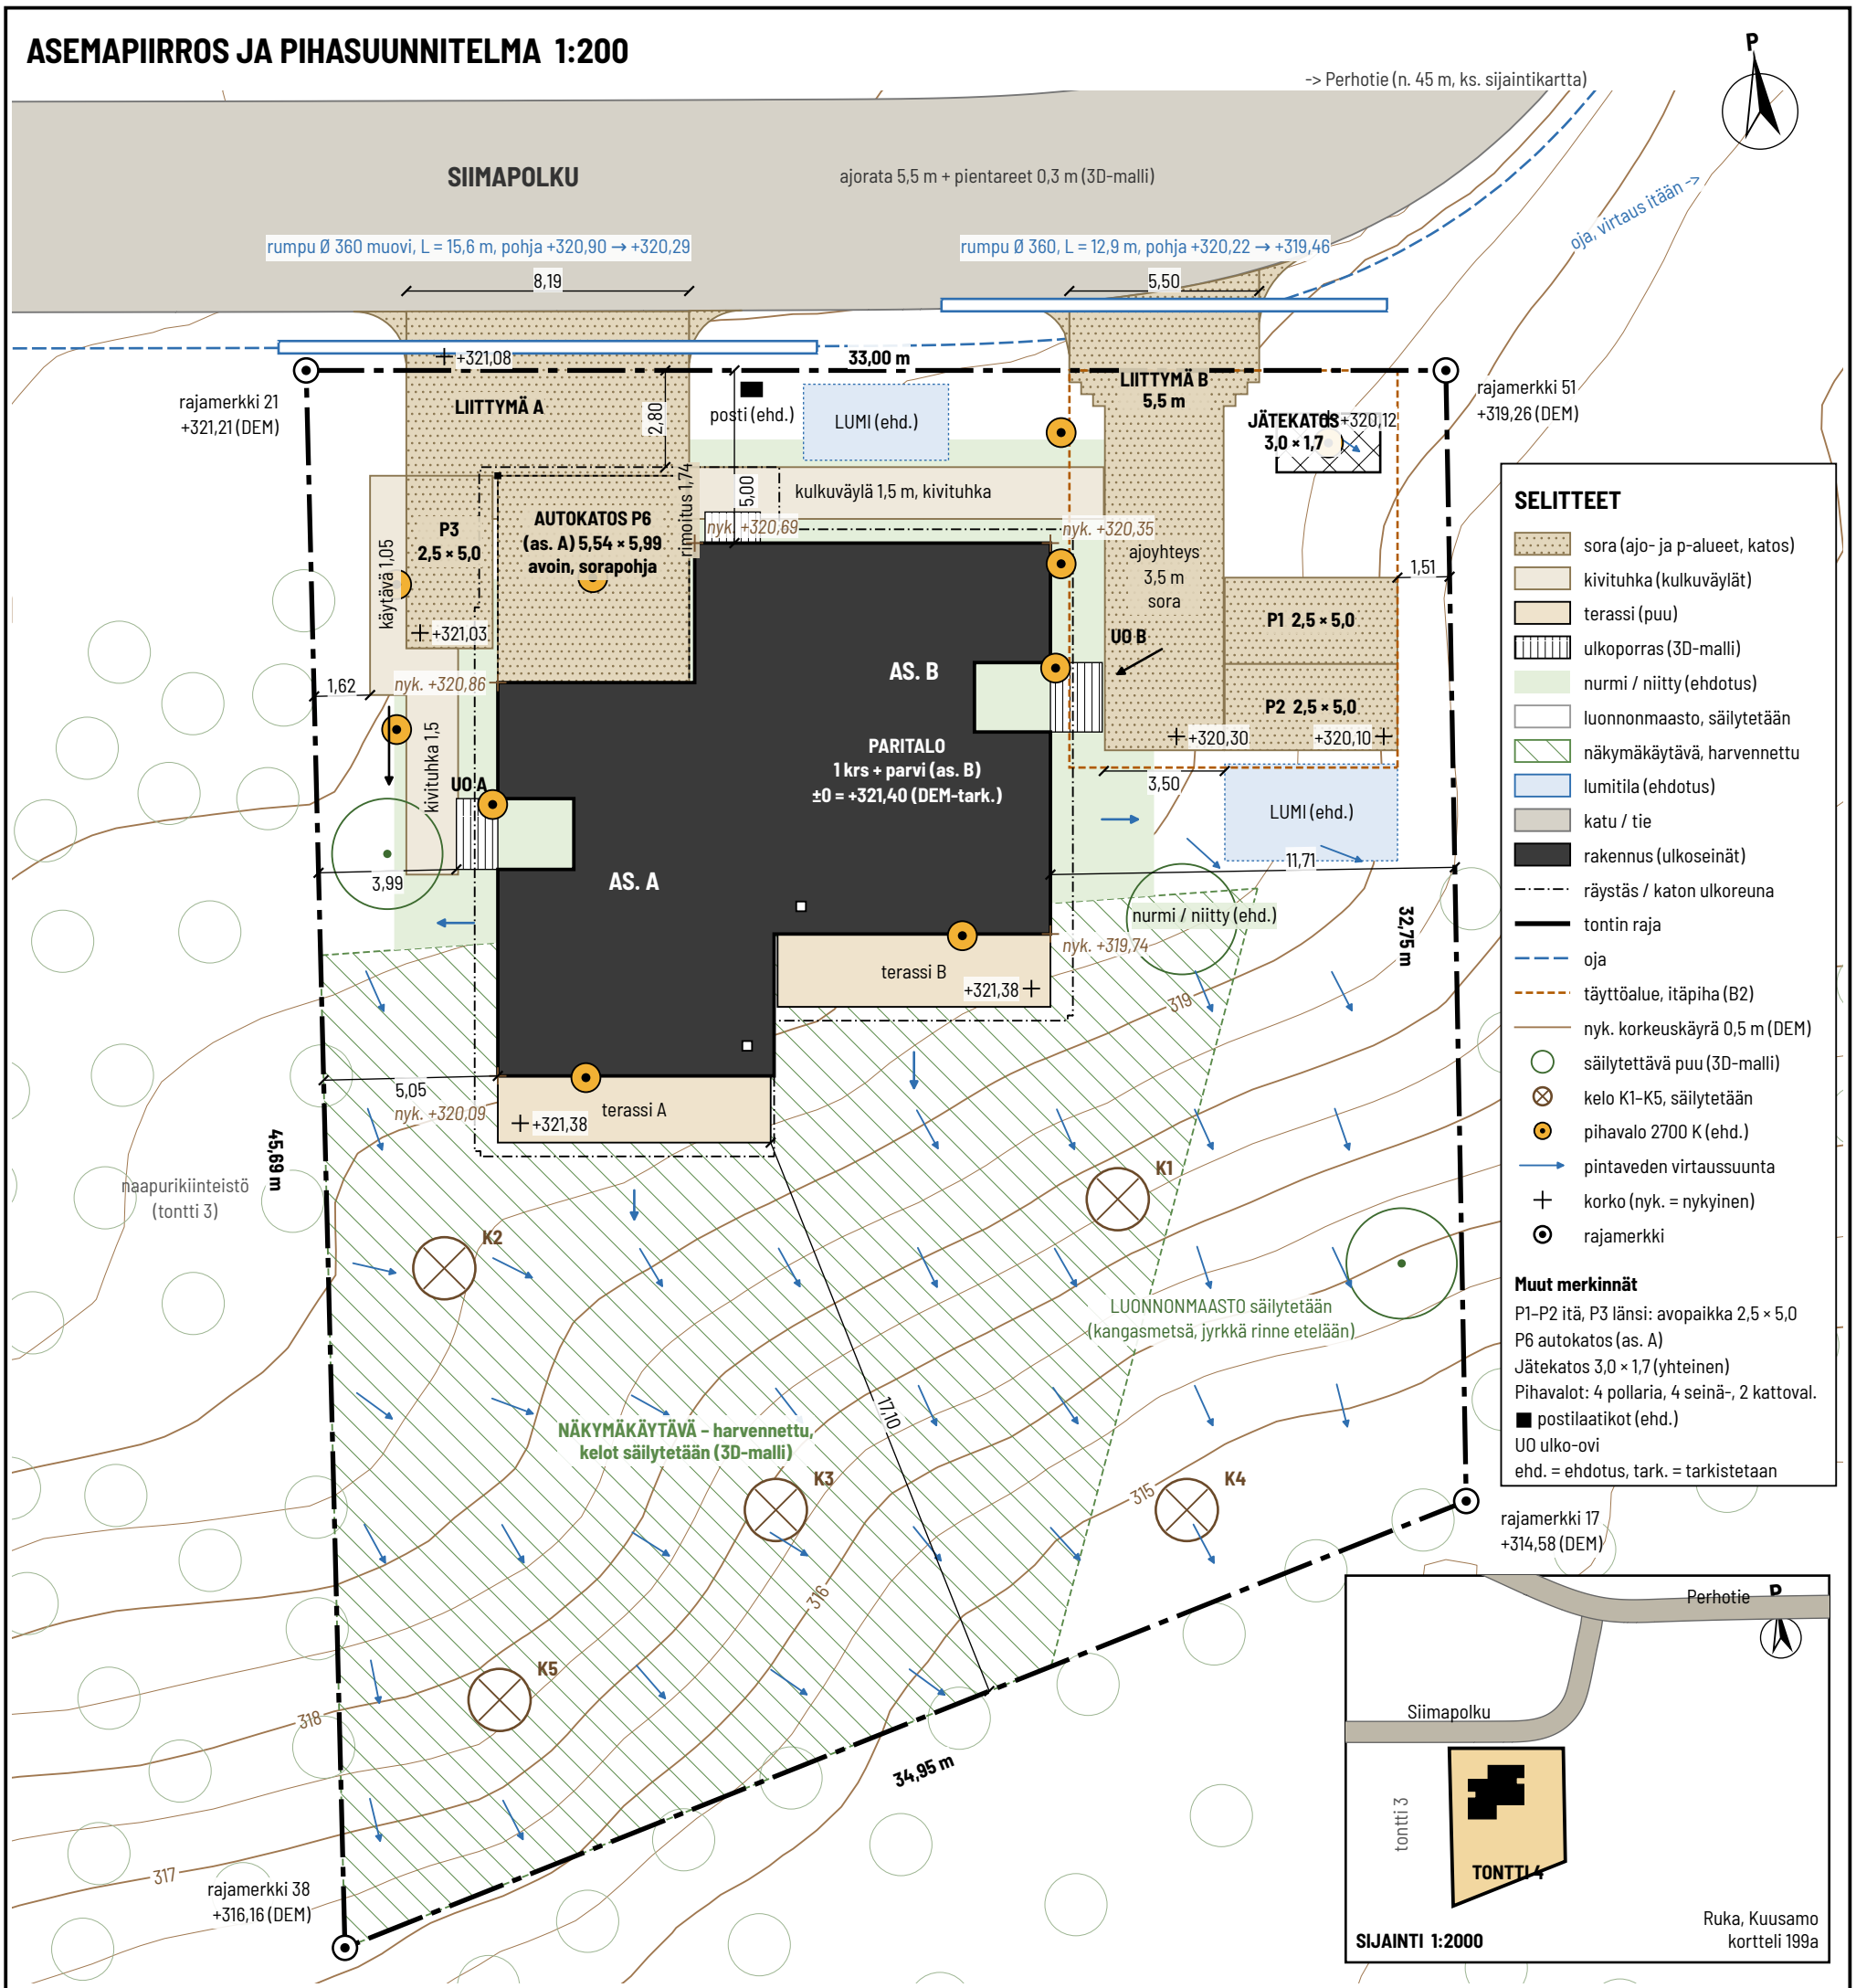

MITTAKAAVA 1:200 (A3)

LUONNOS – ei rakennuslupakelpoinen ennen suunnittelijan tarkastusta ja allekirjoitusta

Korot N2000: MML 2 m DTM (±0,3–0,5 m), kohdistus MML-rajoihin ±0,7 m – tark.
Itäpihan täyttö n. 71 m³ (max 1,2 m, luiska 1:2), taso +320,30…+319,99.
Uusi maanpinta viettää rakennuksesta poispäin (1:20 3 m matkalla); ojat itään.
Ehd. rumpu Siimapolun mutkan alakohtaan (tie +319,4) – tark. RJ: 4 m naapuriin.

RAKENNUSOIKEUS JA ALAT

Kaava / kortteli / tontti	RA (loma-asunnot) · 199a / 4 – tark.
Kiinteistötunnus	305-416-62-90 määräala – tarkistetaan
Tontin pinta-ala	1289 m² (karttamittaus)
Rakennusoikeus	200 k-m² + talousrakennus 40 m²
Kerrosluku / merkintä	½k I u¾ – tulkinta tarkistetaan
Rakennusala	tarkistetaan asemakaavasta
Kerrosala 1. krs (malli / Honka)	182,0 / 183,5 k-m²
Parvi ≥ 1,6 m (as. B)	16,4 k-m²
Kerrosala yhteensä	**198,5 / 199,9 k-m²**
Autokatos (avoin)	33,2 m², ei kerrosalaa – tark.
Tehokkuus e	0,155

ETÄISYYDET (m, 3D-malli)

Katoksen otsa – tieraja	2,80
Varastosiipi / as. B seinä – tieraja	5,00
As. B räystäs – tieraja	4,60
Ulkoseinä – länsiraja (min)	5,05
Räystäs – länsiraja (min)	4,32
Länsiporras – länsiraja	3,99 (< 4,0 – tark.)
Katospilari – länsiraja	5,47
Ulkoseinä – itäraja (min)	11,54
P1–P2 – itäraja (min)	1,51
Terassi – eteläraja (min)	17,10

RAKENNUSKOHDE

Paritalo, 2 loma-asuntoa – Honka Joiku 184, versio B

RAKENNUSPAIKKA / OSOITE	RAKENNUSTOIMENPIDE
Siimapolku, tontti 4 (kortteli 199a), Ruka, Kuusamo – katuosoite tark.	Uudisrakennus

PIIRUSTUKSEN SISÄLTÖ

ASEMAPIIRROS JA PIHASUUNNITELMA

MITTAKAAVA	PÄIVÄYS	VERSIO	PIIRUSTUSNUMERO / LEHTI
1:200	19.10.2026	B2	_____ lehti 3/3


KUNTA / KIINTEISTÖTUNNUS	RAKENNUSLUPATUNNUS
Kuusamo (305) / ____-___-____-____	

PÄÄSUUNNITTELIJA (nimi, tutkinto, allekirjoitus)	RAKENNUSSUUNNITTELIJA (nimi, tutkinto, allekirjoitus)

MUUTOKSET	LÄHTÖTIEDOT
B2 19.10.2026: maasto MML DEM, tiet, rummut, itäpiha; IK1 → 930×1560 B1 19.10.2026: porras KPH-seinä, itä P1–P2 + jätekatos, korkeusaudit	3D-malli tontti4_versio_b.blend (DEM), scene_data_vb_dem MML DEM 2 m (N2000), MML rajat, esite 199a / 4

RAKENNELEIKKAUS B–B 1:50

Koko leveys 15 996 · molemmat lappeet · LUONNOS B1 – ei lupakelpoinen ennen rakennesuunnittelijaa

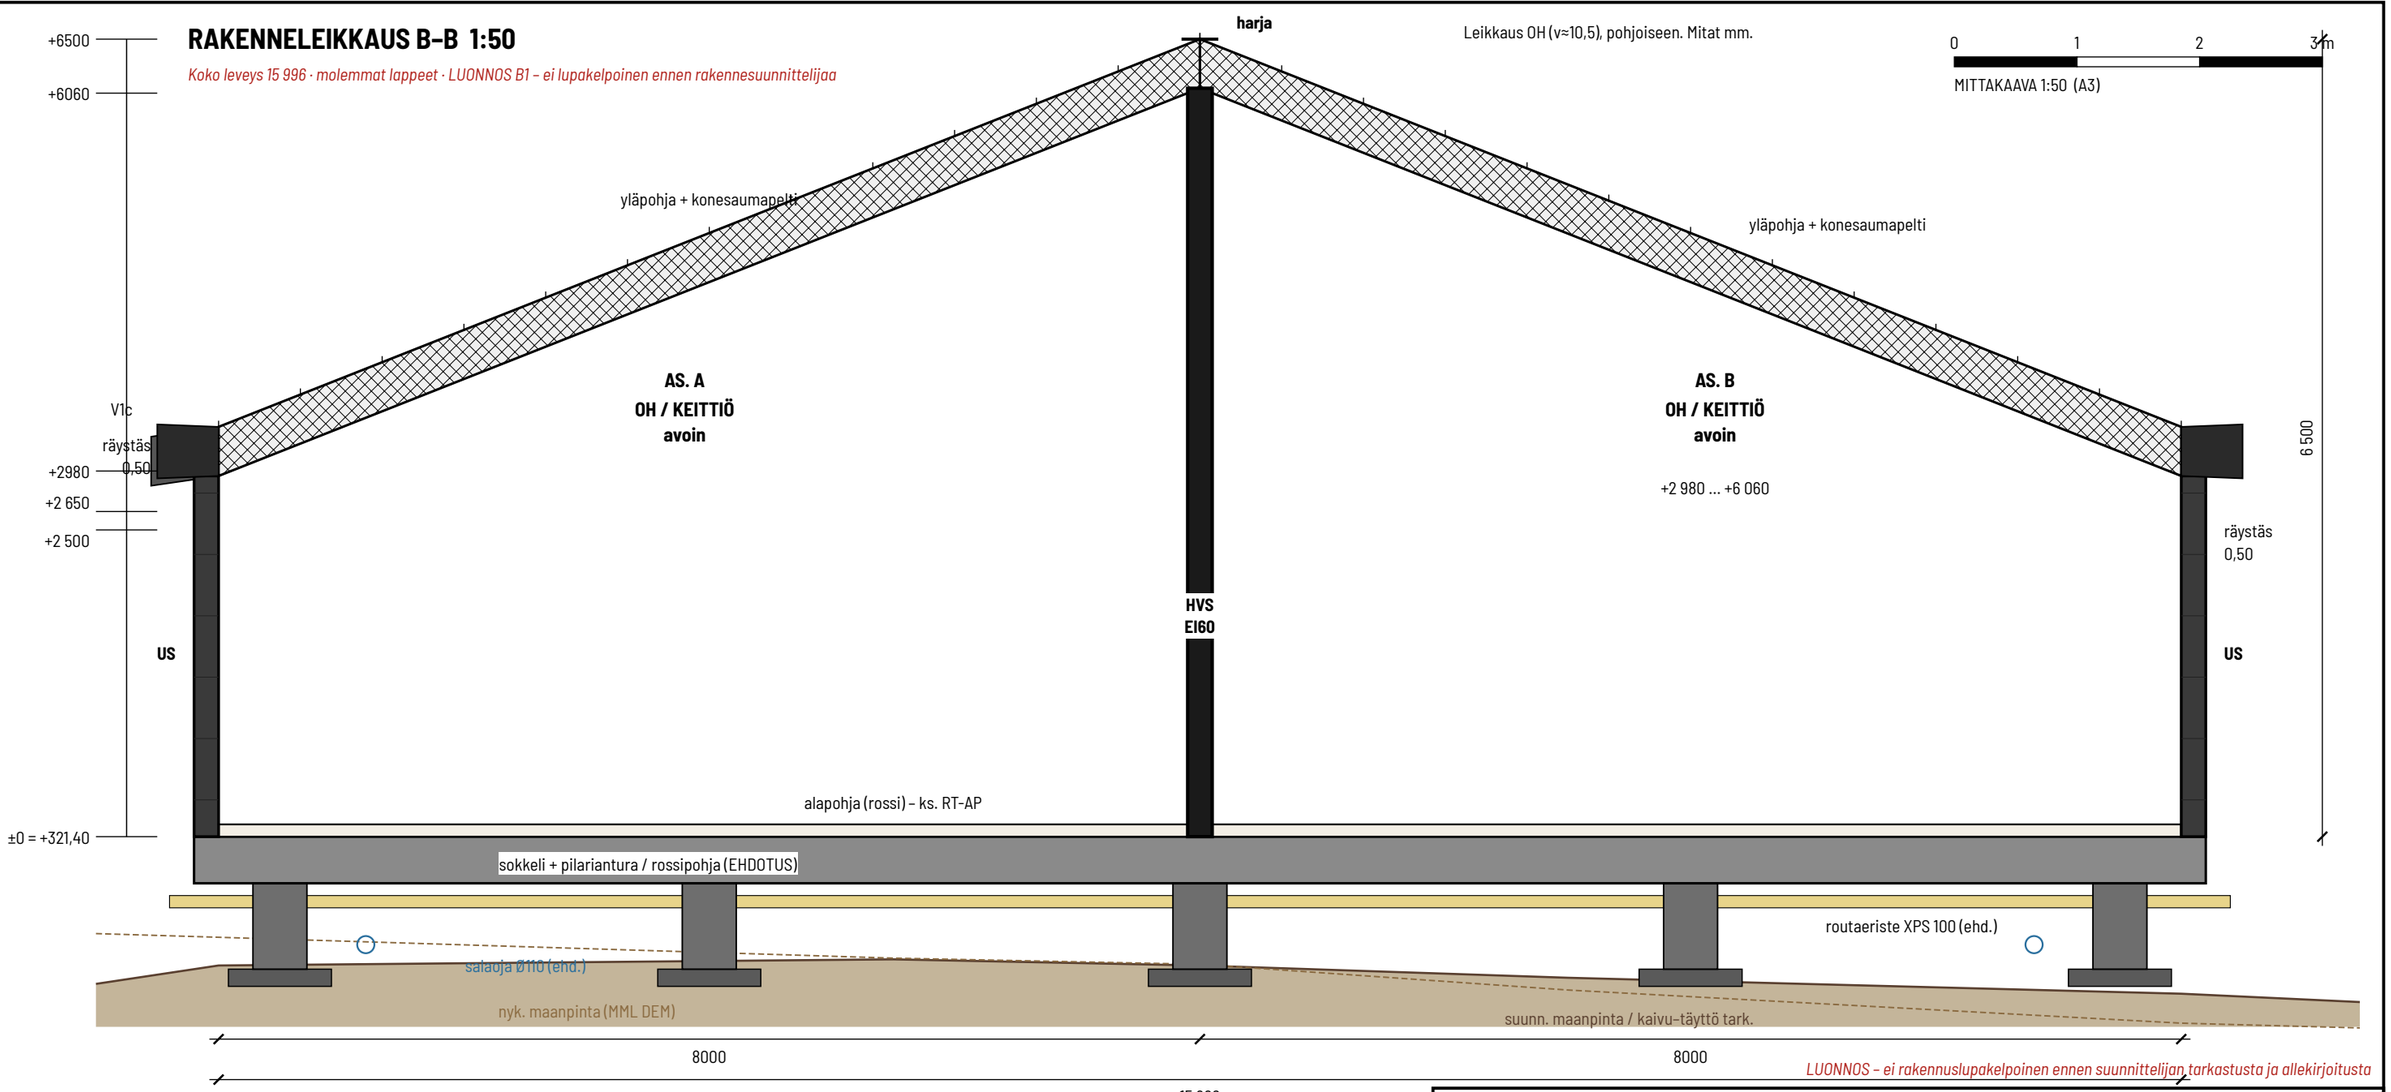


Leikkaus OH (v≈10,5), pohjoiseen. Mitat mm.

0 1 2 3 m
MITTAKAAVA 1:50 (A3)

LUONNOS – ei rakennuslupakelpoinen ennen suunnittelijan tarkastusta ja allekirjoitusta


PARVEN VÄLIPOHJA 1:10 (150 mm, yht. kerrokset 20+25+75+30)

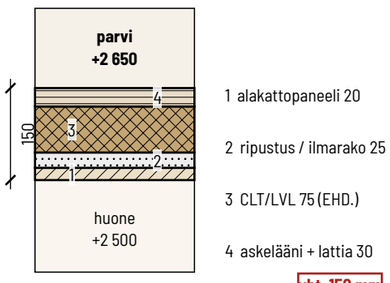

1 alakattopaneeli 20
2 ripustus / ilmarako 25
3 CLT/LVL 75 (EHD.)
4 askeläänі + lattia 30

yht. 150 mm

ULKOSEINÄ 1:20 (sisä→ulko + sokkeli)

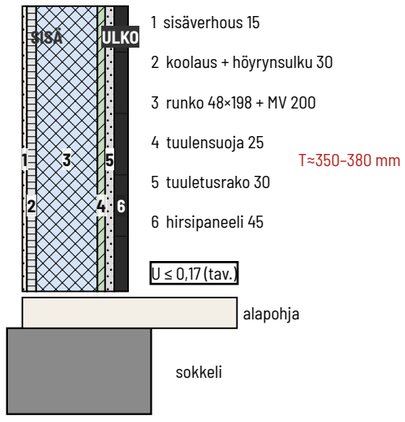

1 sisäverhous 15
2 koolaus + höyrynsulku 30
3 runko 48×198 + MV 200
4 tuulensuoja 25
5 tuuletusrako 30
6 hirsipaneeli 45

T≈350–380 mm

RAKENNETYYPIT (luonnos)

RT-US	sisä15+koolaus/hs30+runko198+MV200+ts25+tuul.30+paneeli45	**U≤0,17**
RT-YP	sisäkatto+hs+eriste≥400+aluskate+tuuletus+konesaumapelti	**U≤0,09**
RT-AP	lattia+palkisto+eriste≥200+tuulettuva ryömintä≥800	**U≤0,16**
RT-VP	lattia30+CLT/LVL75+ripustus25+alakatto20 ≈150	**R'w**
RT-HVS	EI60, R'w≥55 dB – tark. rakennesuunnittelija	**EI60**

Perustus: rossipohja (ehd.). U-arvot tavoite, ei laskentaa.

RAKENNUSKOHDE

Paritalo, 2 loma-asuntoa – Honka Joiku 184, versio B

RAKENNUSPAIKKA / OSOITE	RAKENNUSTOIMENPIDE
Siimapolku, tontti 4 (kortteli 199a), Ruka, Kuusamo – katuosoite tark.	Uudisrakennus

PIIRUSTUKSEN SISÄLTÖ

PÄÄPIIRUSTUS – RAKENNELEIKKAUS B–B 1:50 + DET. 1:5 / 1:20

MITTAKAAVA	PÄIVÄYS	VERSIO	PIIRUSTUSNUMERO / LEHTI
1:50 / 1:5 / 1:20	19.10.2026	B2	_____ lehti 4 / B04

KUNTA / KIINTEISTÖTUNNUS	RAKENNUSLUPATUNNUS
Kuusamo (305) / ____-___-____-____	

PÄÄSUUNNITTELIJA (nimi, tutkinto, allekirjoitus)	RAKENNUSSUUNNITTELIJA (nimi, tutkinto, allekirjoitus)

MUUTOKSET	LÄHTÖTIEDOT
B2 19.10.2026: maasto MML DEM, tiet, rummut, itäpiha; IK1 → 930×1560 B1 19.10.2026: porras KPH-seinä, itä P1–P2 + jätekatos, korkeusaudit	3D-malli tontti4_versio_b.blend (19.10.2026) Honka Joiku 184; mittakaava 24,13 px/m

LIITE – MITOITUSPERUSTEET (Honka Joiku 184 → 3D-malli)

Versio B1 · LUONNOS · 19.10.2026

1. KALIBROINTI: Esitteen ulkoleveys 15 996 mm kiinnitettiin julkisivuarkin vastaavaan pikselileveyteen → mittakaava k = 24,13 px/m (joiku_model.py). Ortovvertailut 2k = 48,26 px/m.
2. POHJA: pohjakuva.png jäljitetty samaan leveyteen; pituus terasseineen 17 361 mm. Harja/huoneistoseinä u = 8,0.
3. KORKEUDET JULKISIVUISTA (maasta): lattia +0,50 · räystäs ylä +3,85 · harja +7,00 → kaltevuus 21,6°. Sisäkatto harjalla ~+6,06 (lattia ±0). Vertailu: oviaukko ~2,1 m, pohjoisikkuna 0,93×2,65.
4. OLETUKSET: alakatto MH/eteinen/keittiö +2,50; KPH/WC +2,40; sauna +2,20; parvi PF +2,65 / PS +2,50 (150 mm). Ulkoseinä T=200 mm mallissa on visuaalinen; todellinen runko+paneeli paksumpi (ks. B04).
5. EPÄVARMUUS: pohja ±50…100 mm; korkeudet ±100…200 mm (rasteri). Rakennepaksuudet = ehdotus.
6. KERROSALA: Honka 183,5 + parvi ≥1,6 m (16,44) = 199,94 k-m² ≤ 200.
7. Lähdekuvat: /workspace/3d/joiku/ref/julkisivut.png, etela_x3.png; /workspace/havainne/ref/pohjakuva.png, honka_*.jpg.


Julkisivuarkki + kalibrointiselite



MITTAUSPERUSTE (kalibrointi)

Lähdekuva: julkisivut.png 1000×560 px + etela_x3.png / pohjoinen_x3.png (suurennetut rajaukset)
Kalibrointi: Honka-leveys 15 996 mm → mittakaava k = 24,13 px/m (joiku_model.py).
Tarkistus: 15,996 m × 24,13 px/m = 386.0 px (yksittäisen julkisivun leveys lähdearkilla).
Korkeus: lattia/sokkelin ylä +0,50 m maasta; räystään ylä +3,85; harja +7,00 → kaltevuus atan(0,395)=21,6°.
Vertailuarvot: oviaukko ~2,1 m; pohjoisikkuna 0,93×2,65 (lasi +0,76…+3,41); sivuräystäs 0,50–0,60 m.
Epävarmuus: ±0,05…0,10 m pohjamitoissa; ±0,10…0,20 m korkeuksissa (pikselimittakaava + rasterointi).

Eteläjulkisivu – korkeusviivat (havainnollistus)

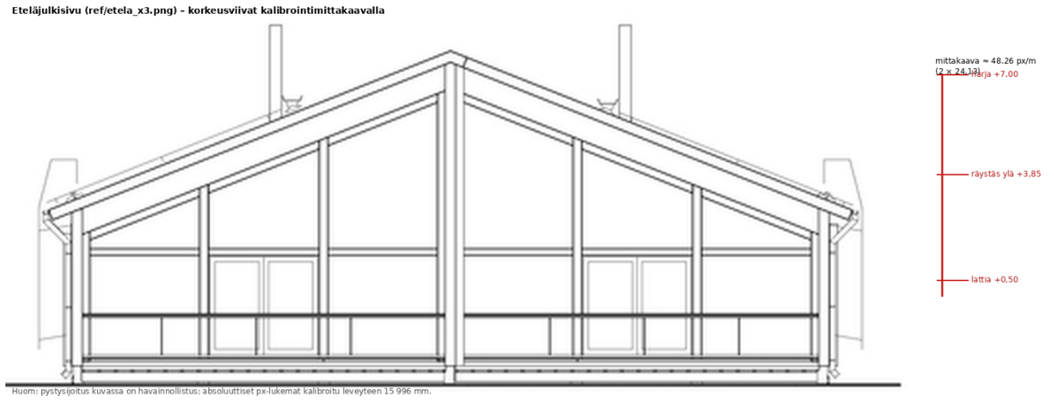

LUONNOS – ei rakennuslupakelpoinen ennen suunnittelijan tarkastusta ja allekirjoitusta

RAKENNUSKOHDE **Paritalo – Honka Joiku 184, versio B**			
RAKENNUSPAIKKA / OSOITE Siimapolku, tontti 4, Ruka, Kuusamo		RAKENNUSTOIMENPIDE Uudisrakennus	
PIIRUSTUKSEN SISÄLTÖ **LIITE – MITOITUSPERUSTEET (lähdekuvat → 3D-malli)**			
MITTAKAAVA –	PÄIVÄYS 19.10.2026	VERSIO B1	PIIRUSTUSNUMERO / LEHTI _____ liite M1
KUNTA / KIINTEISTÖTUNNUS Kuusamo (305) / ____-___-____-____		RAKENNUSLUPATUNNUS	
PÄÄSUUNNITTELIJA (nimi, tutkinto, allekirjoitus)		RAKENNUSSUUNNITTELIJA (nimi, tutkinto, allekirjoitus)	
MUUTOKSET B1 19.10.2026: porras KPH-seinä, itä P1–P2 + jätekatos, korkeusaudit		LÄHTÖTIEDOT julkisivut.png, pohjakuva.png, esite 183,5 m² / 15 996 mm	